


01 FRONT ELEVATION

Bench / stepped ledge with curved transition · 1:20

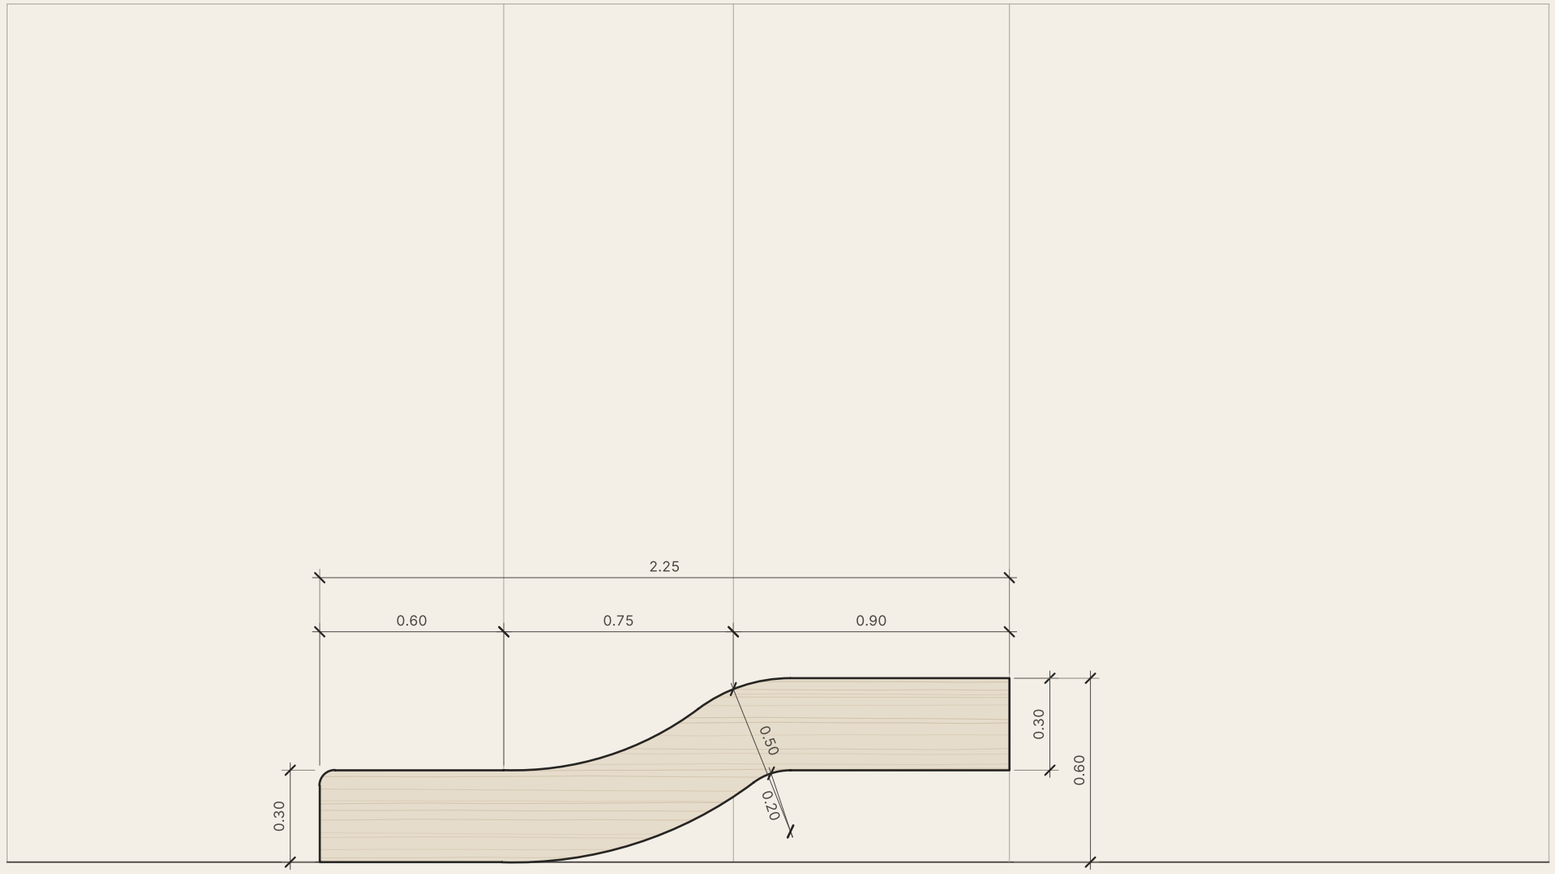



REFERENCE Form and material intent

DESIGN DEVELOPMENT

Bespoke Furniture

Stone furniture collection

SHEET

Bench

Front elevation

DRAWING INDEX

DD-01 Bench — elevation
DD-02 Dining table — plan
DD-03 Coffee table — plan & elevation

NOTES

Wall lines shown for context only;
panel joints align with bench set-out.
Inclined dimensions 0.50 and 0.20 are
measured along the dimension lines shown.
Edge radii as drawn.

LINE KEY

- Furniture outline
- Secondary / internal edge
- Context (wall, chairs, floor)
- Dimension / extension line

MATERIAL (INDICATIVE)

Travertine

Finish & grade to be confirmed — refer reference imagery

CLIENT
—

PROJECT NO.
—

ISSUE
Design development


DATE
03.11.2026

REVISION
P01

UNITS
Metres

DD-01

SCALE
1:20 @ A3

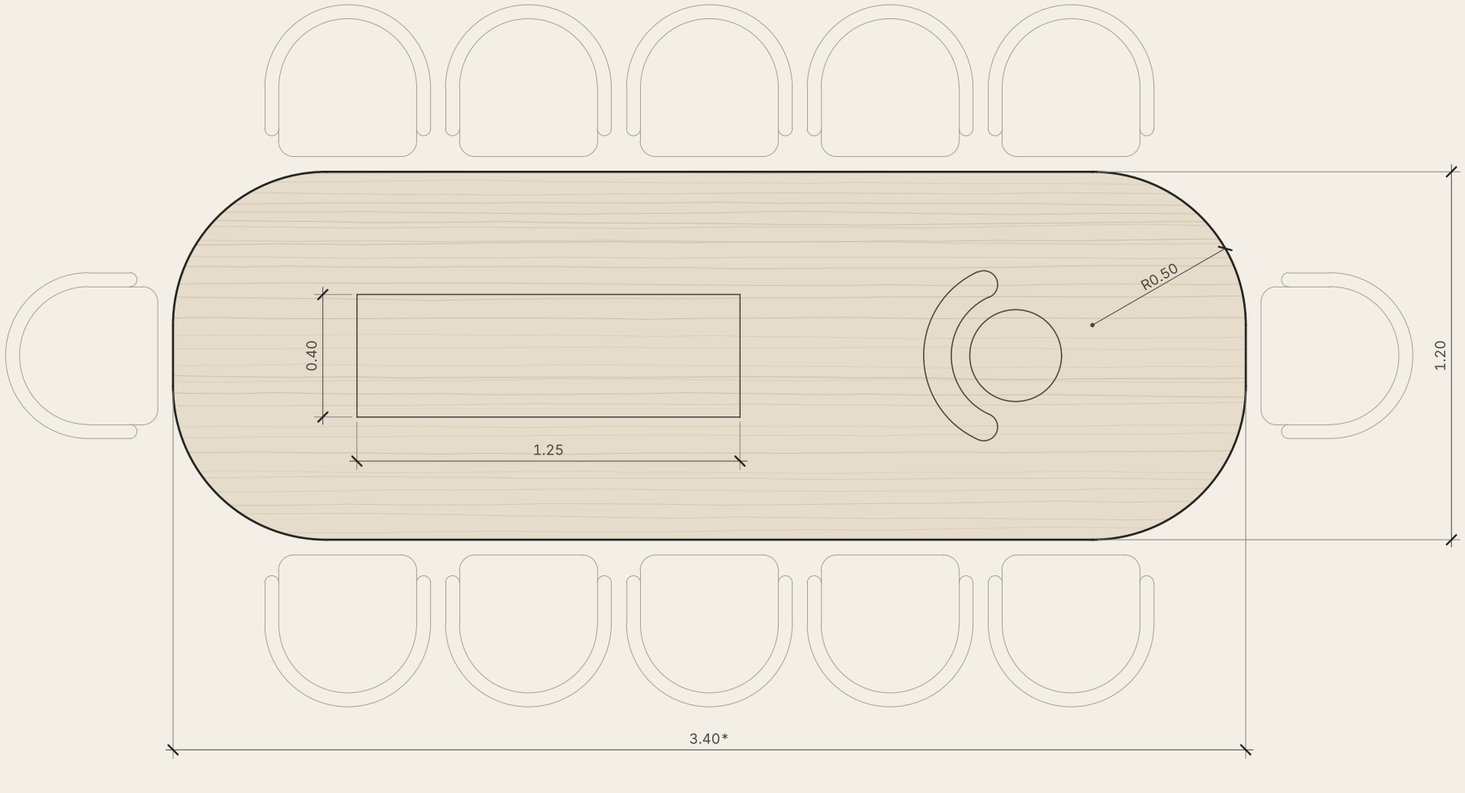

02 **PLAN**

Dining table with 12 chairs · 1:20





REFERENCE Form and material intent

DESIGN DEVELOPMENT

Bespoke Furniture

Stone furniture collection

SHEET

Dining table

Plan

DRAWING INDEX

DD-01 Bench — elevation
DD-02 Dining table — plan
DD-03 Coffee table — plan & elevation

NOTES

Internal outlines indicate pedestal and leg footprints below the top, as drawn.

Leg positions and sizes not dimensioned — shown as drawn, not to be scaled.

Chairs indicative of layout only.

* Overall length — to be confirmed

Written dimension is 3.40. The drawn outline (R0.50 ends, 1.20 wide) scales to 3.50.

Geometry reproduced unaltered from source.

LINE KEY

- Furniture outline
- Secondary / internal edge
- Context (wall, chairs, floor)
- Dimension / extension line

MATERIAL (INDICATIVE)

Travertine

Finish & grade to be confirmed — refer reference imagery

CLIENT
—

PROJECT NO.
—

ISSUE
Design development


DATE
03.11.2026

REVISION
P01

UNITS
Metres

DD-02

SCALE
1:20 @ A3

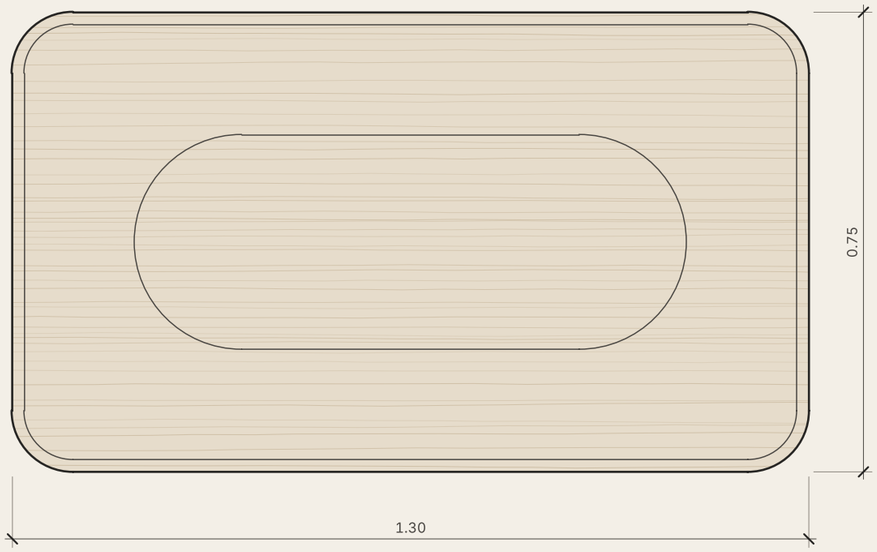


03 **PLAN**

Coffee table · 1:10



REFERENCE Form and material intent

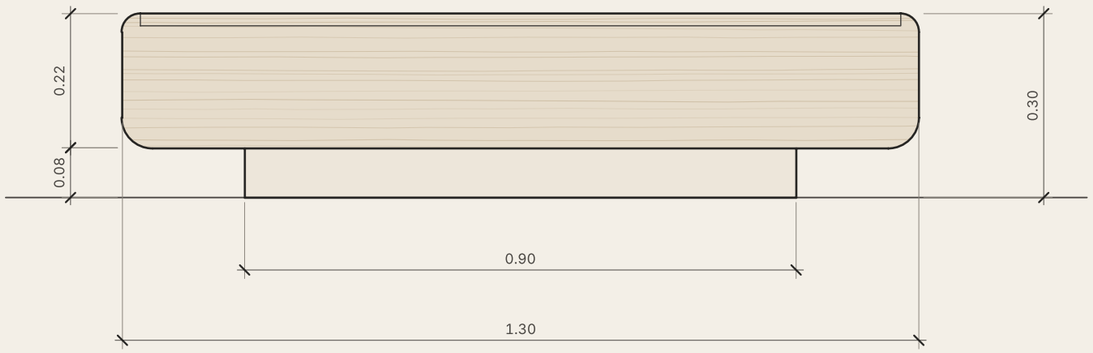

04 **ELEVATION**

Coffee table — top on recessed plinth · 1:10



DESIGN DEVELOPMENT

Bespoke Furniture

Stone furniture collection

SHEET

Coffee table

Plan & elevation

DRAWING INDEX

DD-01	Bench — elevation
DD-02	Dining table — plan
DD-03	Coffee table — plan & elevation

NOTES

Elevation projected directly from plan. Inner rounded outline in plan aligns with the 0.90 plinth in elevation (not separately dimensioned). Edge line and corner radii as drawn.

LINE KEY

- Furniture outline
- Secondary / internal edge
- Context (wall, chairs, floor)
- Dimension / extension line

MATERIAL (INDICATIVE)

Travertine

Finish & grade to be confirmed — refer reference imagery

CLIENT
—

PROJECT NO.
—

ISSUE
Design development

DATE
03.11.2026

REVISION
P01

UNITS
Metres

DD-03

SCALE
1:10 @ A3